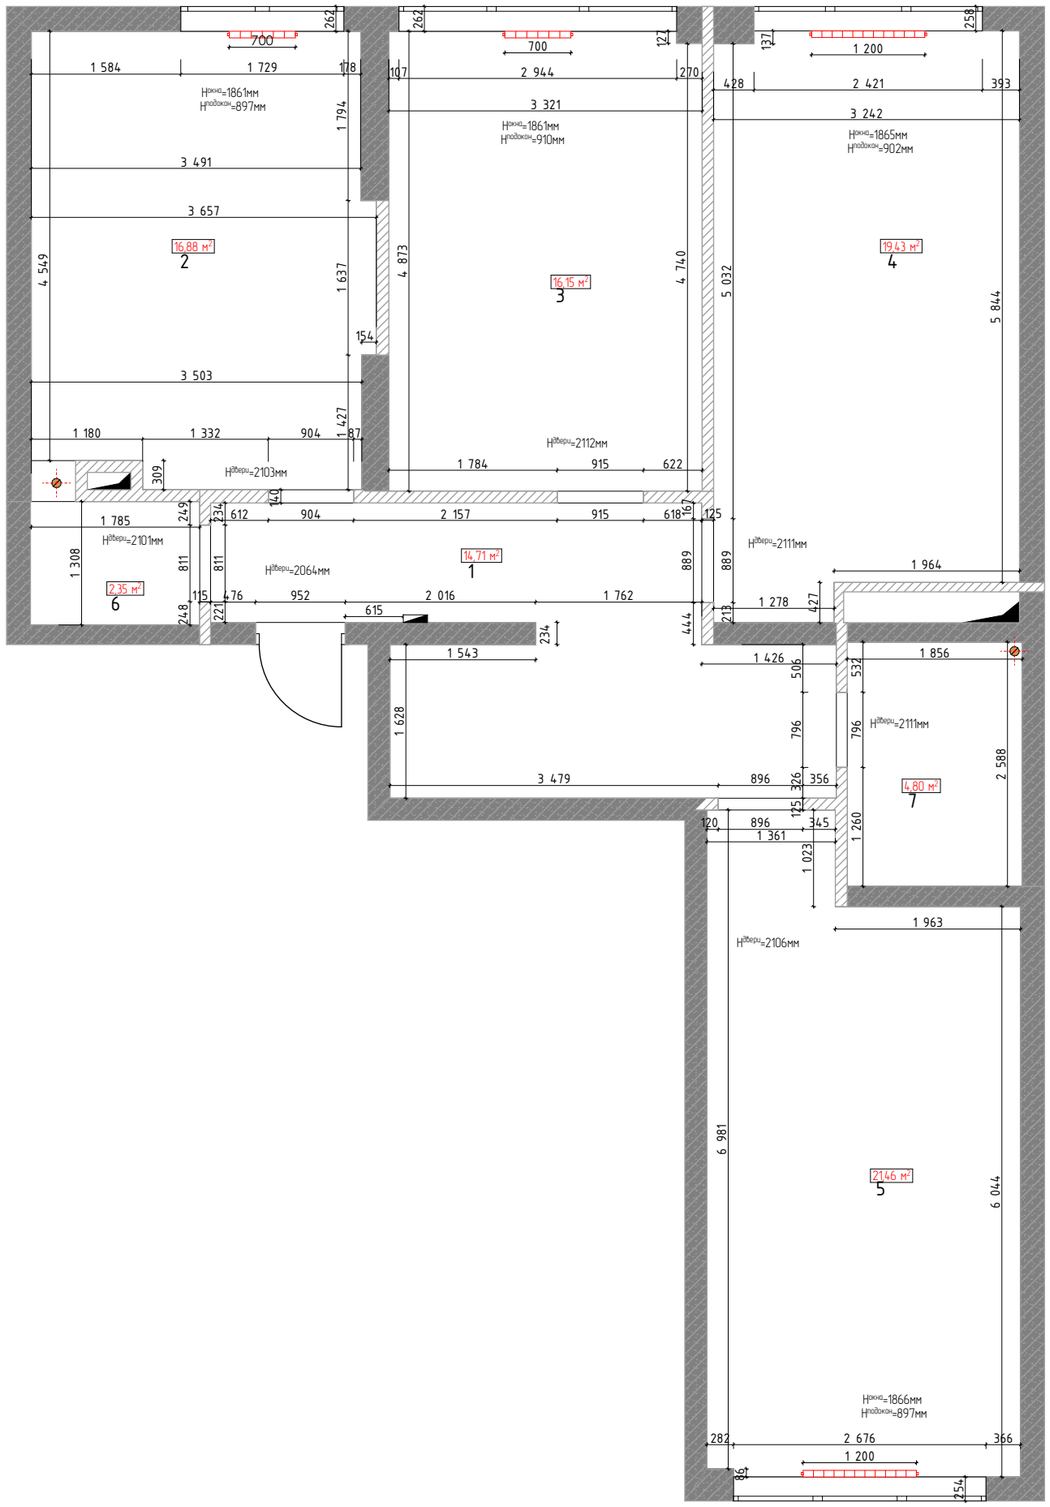


Условные обозначения	
2D Вид	Наименование
	Стены существующие несущие
	Стены существующие не несущие/газоблок
	Вентиляц. шахта
	Коммуникации
	Радиатор отопления
	Эл.щиток

№	Наименование	Площадь
1	Прихожая	14,71 м²
2	Комната 1	16,88 м²
3	Комната 2	16,15 м²
4	Комната 3	19,43 м²
5	Комната 4	21,46 м²
6	Санузел	2,35 м²
7	Ванная	4,80 м²
	Высота потолков	2760 мм
	Общая площадь	95,78 м²

Примечание:
Все размеры указаны в миллиметрах и носят рекомендательный характер.
Уточнять все размеры на месте со смежником

Изм.	Лист	№ Докум.	Подпись	Дата	Дизайн-проект технический			
Разраб.		Азимова С.М.			Обмерный план М:65	Лит.	Лист	Листов
Рук.проекта								
							ОСНОВА	